НОРНИКЕЛЬ
КОЛЬСКАЯ ГМК

г. Мончегорск

ПРИ ПОЖАРЕ ЗВОНИТЬ

телефон АСС 90-01
с мобильного *90-01

ПЛАН ЭВАКУАЦИИ

ЗДАНИЕ СТОЛОВОЙ

подвал


УТВЕРЖДАЮ

_____

_____

_____

"____" _____ 202_ г.

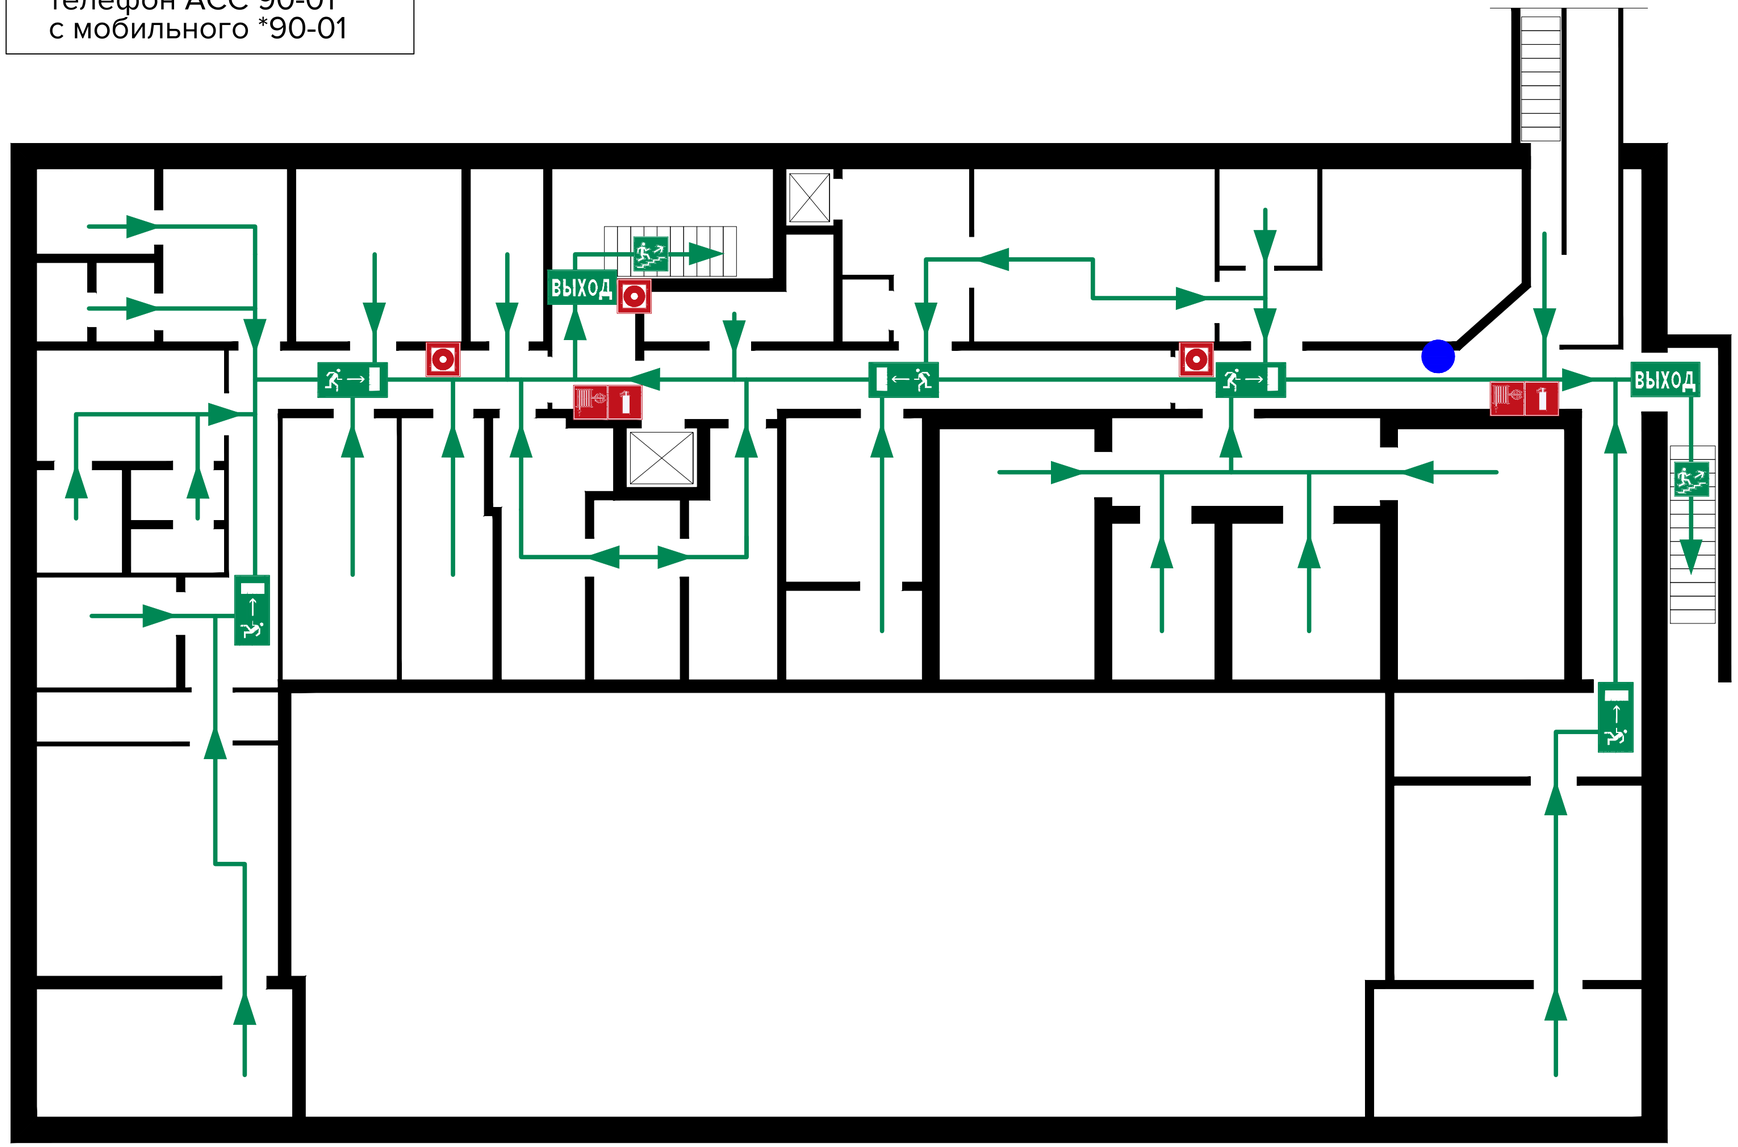

ДЕЙСТВИЯ ПРИ ПОЖАРЕ: СОХРАНЯЙТЕ СПОКОЙСТВИЕ	
1 СООБЩИТЬ ПО ТЕЛЕФОНУ тел. АСС 90-01 с моб. *90-01	• АДРЕС ОБЪЕКТА • МЕСТО ВОЗНИКНОВЕНИЯ ПОЖАРА • СВОЮ ФАМИЛИЮ • ПРИВЕСТИ В ДЕЙСТВИЕ СИСТЕМУ ПОЖАРНОЙ СИГНАЛИЗАЦИИ
2 ЭВАКУИРОВАТЬ ЛЮДЕЙ	• ОРИЕНТИРОВАТЬСЯ ПО ЗНАКАМ НАПРАВЛЕНИЯ ДВИЖЕНИЯ • ВЗЯТЬ С СОБОЙ ПОСТРАДАВШИХ • ОКАЗАТЬ ПОМОЩЬ ПОСТРАДАВШИМ
3 ПРИНЯТЬ МЕРЫ ПО ТУШЕНИЮ ПОЖАРА	• ИСПОЛЬЗОВАТЬ СРЕДСТВА ПРОТИВОПОЖАРНОЙ ЗАЩИТЫ • ПРИ НЕОБХОДИМОСТИ ОБЕСТОЧИТЬ ПОМЕЩЕНИЕ

ИНФОРМАЦИЯ:
СПОСОБ ОПОВЕЩЕНИЯ АВТОМАТИЧЕСКИЙ ЧЕРЕЗ РЕЧЕВУЮ СИСТЕМУ ОПОВЕЩЕНИЯ И УПРАВЛЕНИЯ ЭВАКУАЦИЕЙ ЛЮДЕЙ ПРИ ПОЖАРЕ , А ТАК ЖЕ ВРУЧНУЮ, ИСПОЛЬЗУЯ ВНУТРЕННЮЮ ГРОМКУЮ СВЯЗЬ СИСТЕМЫ ТЕХНОЛОГИЧЕСКОГО ОПОВЕЩЕНИЯ.
ЗАПУСК В РУЧНОМ РЕЖИМЕ АВТОМАТИЧЕСКОЙ СИСТЕМЫ ОПОВЕЩЕНИЯ И УПРАВЛЕНИЯ ЭВАКУАЦИИ ЛЮДЕЙ ПРИ ПОЖАРЕ ПРОИЗВОДИТСЯ ОТ РУЧНЫХ ПОЖАРНЫХ ИЗВЕЩАТЕЛЕЙ, УСТАНАНОВЛЕННЫХ НА СТЕНАХ ВБЛИЗИ ЭВАКУАЦИОННЫХ ВЫХОДОВ.
МЕСТА РАСПОЛОЖЕНИЯ ПОЖАРНЫХ ИЗВЕЩАТЕЛЕЙ ОБОЗНАЧЕНЫ НА НАСТОЯЩЕМ ПЛАНЕ

ДЕЙСТВИЯ ПРИ АВАРИИ: СОХРАНЯЙТЕ СПОКОЙСТВИЕ	
1 СООБЩИТЬ ПО ТЕЛЕФОНУ тел. АСС 90-01 с моб. *90-01	• АДРЕС ОБЪЕКТА • МЕСТО ВОЗНИКНОВЕНИЯ АВАРИИ • СВОЮ ФАМИЛИЮ • ПРИВЕСТИ В ДЕЙСТВИЕ СИСТЕМУ ПОЖАРНОЙ СИГНАЛИЗАЦИИ
2 ЭВАКУИРОВАТЬ ЛЮДЕЙ	• ОРИЕНТИРОВАТЬСЯ ПО ЗНАКАМ НАПРАВЛЕНИЯ ДВИЖЕНИЯ • ВЗЯТЬ С СОБОЙ ПОСТРАДАВШИХ • ОКАЗАТЬ ПОМОЩЬ ПОСТРАДАВШИМ
3 ПРИНЯТЬ МЕРЫ ПО ЛИКВИДАЦИИ АВАРИИ	• ИСПОЛЬЗОВАТЬ СРЕДСТВА ЗАЩИТЫ • ПРЕДОТВРАТИТЬ РАЗВИТИЕ АВАРИИ • ОБОЗНАЧИТЬ МЕСТО АВАРИИ

УСЛОВНЫЕ ОБОЗНАЧЕНИЯ:	
ВЫХОД ЭВАКУАЦИОННЫЙ ВЫХОД	ТЕЛЕФОН
ПУТЬ К ЭВАКУАЦИОННОМУ ВЫХОДУ	ПОЖАРНЫЙ КРАН
НАПРАВЛЕНИЕ ДВИЖЕНИЯ К ЭВАКУАЦИОННОМУ ВЫХОДУ	ОГНЕТУШИТЕЛЬ
НАПРАВЛЕНИЕ ДВИЖЕНИЯ К ВЫХОДУ ПО ЛЕСТНИЦЕ ВНИЗ	КНОПКА ВКЛЮЧЕНИЯ ПОЖАРНОЙ АВТОМАТИКИ
АПТЕЧКА ЭЛЕКТРОЩИТОВАЯ	ВЫ НАХОДИТЕСЬ ЗДЕСЬ

ИЗГОТОВИТЕЛЬ: ИП АНДРЕЕВ А. А. ФП-24 - 2024/ 200-25-1440 ГОСТ 34428-2018-Е